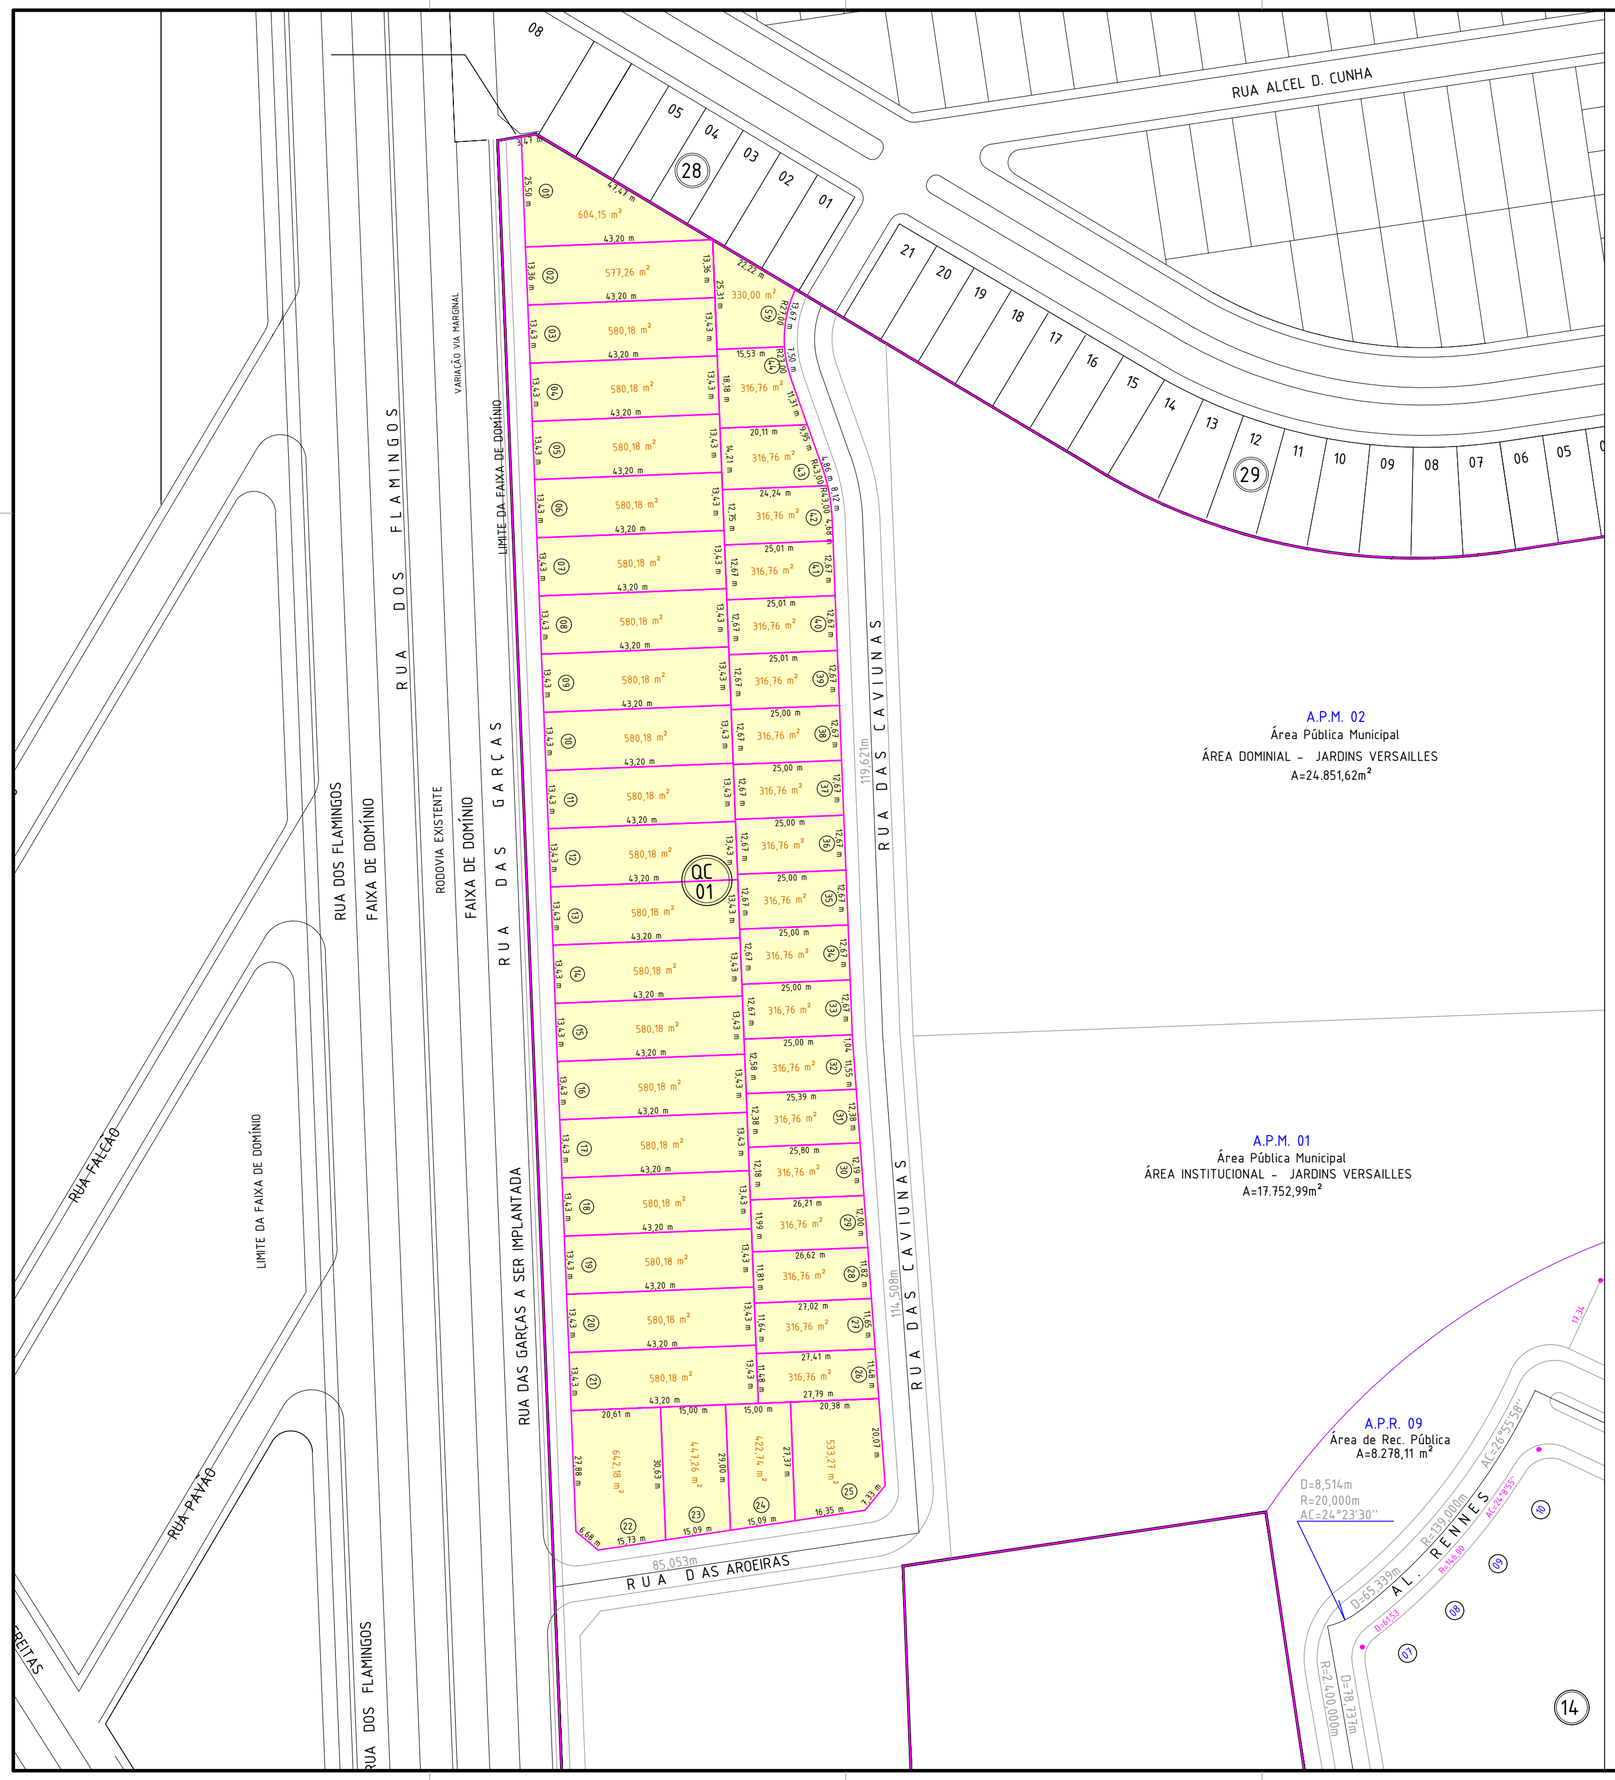

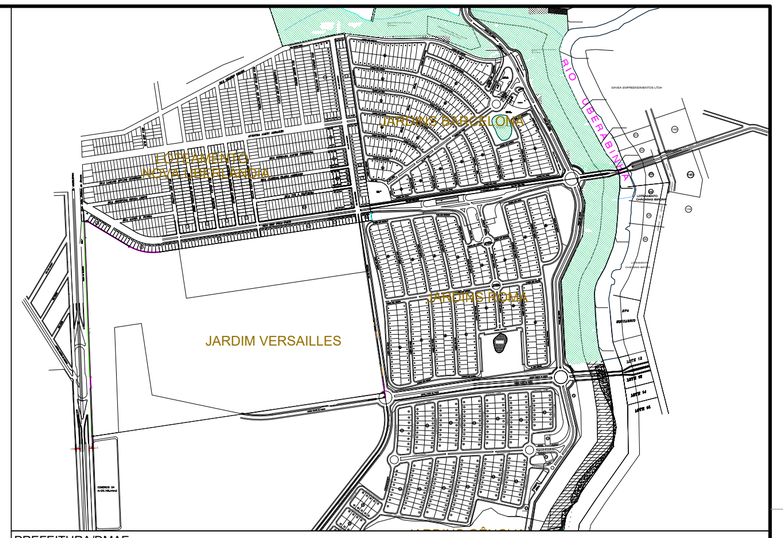

PREFEITURA/DMAE

OBSERVAÇÕES:

DATA	REVISÃO	ALTERAÇÃO
19/10/2023	00	EMISSÃO INICIAL
05/11/2024	01	NOVAS PROPOSTAS DE DESDOBRO
18/11/2024	02	NOVA PROPOSTA DE DESDOBRO

TÍTULO:
ESTUDO DESDOBRO QUADRA C1 - JARDIM VERSAILLES

DATA:
18/11/2024

LOCAL:
LOTEAMENTO FECHADO HABITACIONAL JARDIM VERSAILLES

CIDADE:
UBERLÂNDIA - MG

PROPRIETÁRIO:
CIDADE JARDIM SPE

ESCALA:
1:1000

OBJETIVO:
ESTUDO DESDOBRO QUADRA C1

FOLHA:
ÚNICA

CONTEÚDO:
PLANTA BAIXA

RS ENGENHARIA
INFRAESTRUTURA URBANA
DIRETOR COMERCIAL
SILVIO SIMÕES
CREA-MG: 92238/D
(34) 9 8428.2140
DIRETOR TÉCNICO
TULIO RIBEIRO
CREA-MG: 207690/D
(34) 9 8878.6801
topografia@ribeirosimoeseng.com
ribeirosimoesengenharia.com

ASSINATURAS:

CIDADE JARDIM SPE
15.522.298/00001-77

TULIO RIBEIRO DE QUEIROZ
CREA-MG 207.690/D

ÁREA:
-

DESENHO:
ANA CAROLINA B

ARQUIVO BASE:
CALCULO_URBANÍSTICO_JARDIM_VERSAILLES_05-09-14

REVISÃO:
02